

TOPORAY


Levantamientos topográficos



Levantamiento sin nombre

Estación inicial: E 1000.000 / N 1000.000

Fecha: 17/7/2026 · Formato A3 horizontal · Escala 1:1000 · Área total: 20838.268 m² · Perímetro / longitud: 711.756 m

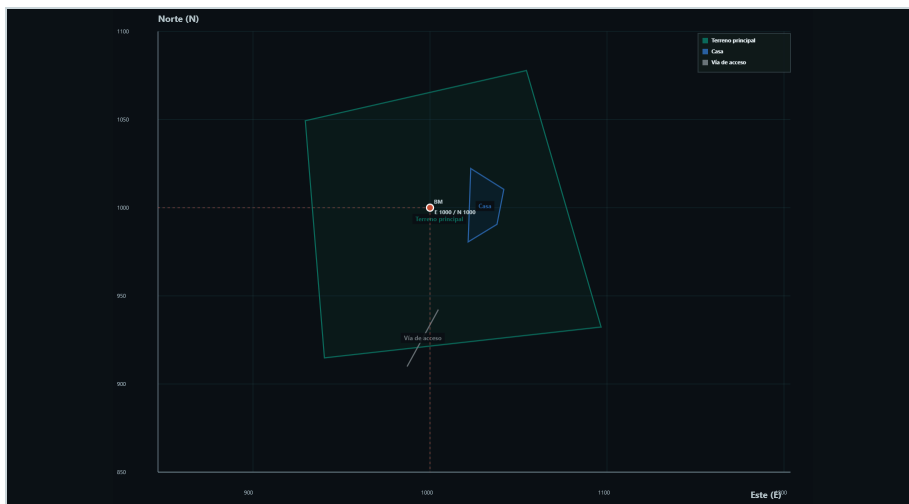

Resumen por zonas

Zona	Tipo	Puntos	Área (m²)	Perímetro / longitud (m)
Terreno principal	Polígono	4	20298.000	571.875
Casa	Polígono	4	540.268	103.102
Vía de acceso	Línea	2	0.000	36.779

Puntos y resultados

Punto	DATOS		AZIMUT			DIST.	E-Sen-W	N-Cos-S	RUMBO					PROYECCIONES				COORDENADAS		PERÍMETRO	
	Zona	Descripción	GG	MM	SS				N-S	gg	mm	ss	E-W	N(+)	S(-)	E(+)	W(-)	N	E	Dist.	d[P-P(+1)]
BM	Referencia	Coordenada inicial															1000.000	1000.000			
1	Terreno principal	Esquina norte	35	0	0	95.000	0.573576	0.819152	N	35	0	0	E	77.819		54.490		1077.819	1054.490	151.489	d1-2
2	Terreno principal	Esquina este	125	0	0	118.000	0.819152	-0.573576	S	55	0	0	E		67.682	96.660		932.318	1096.660	157.290	d2-3
3	Terreno principal	Esquina sur	215	0	0	104.000	-0.573576	-0.819152	S	35	0	0	W		85.192		59.652	914.808	940.348	134.952	d3-4
4	Terreno principal	Esquina oeste	305	0	0	86.000	-0.819152	0.573576	N	55	0	0	W	49.328			70.447	1049.328	929.553	128.144	d4-1
1	Casa	Casa 1	46	0	0	32.000	0.719340	0.694658	N	46	0	0	E	22.229		23.019		1022.229	1023.019	22.129	d1-2
2	Casa	Casa 2	76	0	0	43.000	0.970296	0.241922	N	76	0	0	E	10.403		41.723		1010.403	1041.723	20.214	d2-3
3	Casa	Casa 3	104	0	0	39.000	0.970296	-0.241922	S	76	0	0	E		9.435	37.842		990.565	1037.842	19.099	d3-4
4	Casa	Casa 4	132	0	0	29.000	0.743145	-0.669131	S	48	0	0	E		19.405	21.551		980.595	1021.551	41.660	d4-1
1	Vía de acceso	Inicio de vía	175	20	0	58.000	0.081359	-0.996685	S	4	40	0	E		57.808	4.719		942.192	1004.719	36.779	d1-2
2	Vía de acceso	Final de vía	188	10	0	91.000	-0.142053	-0.989859	S	8	10	0	W		90.077		12.927	909.923	987.073		

Perímetro / longitud total: 711.756 m

Contacto: Carlos Martinez
Celular: 3138219745